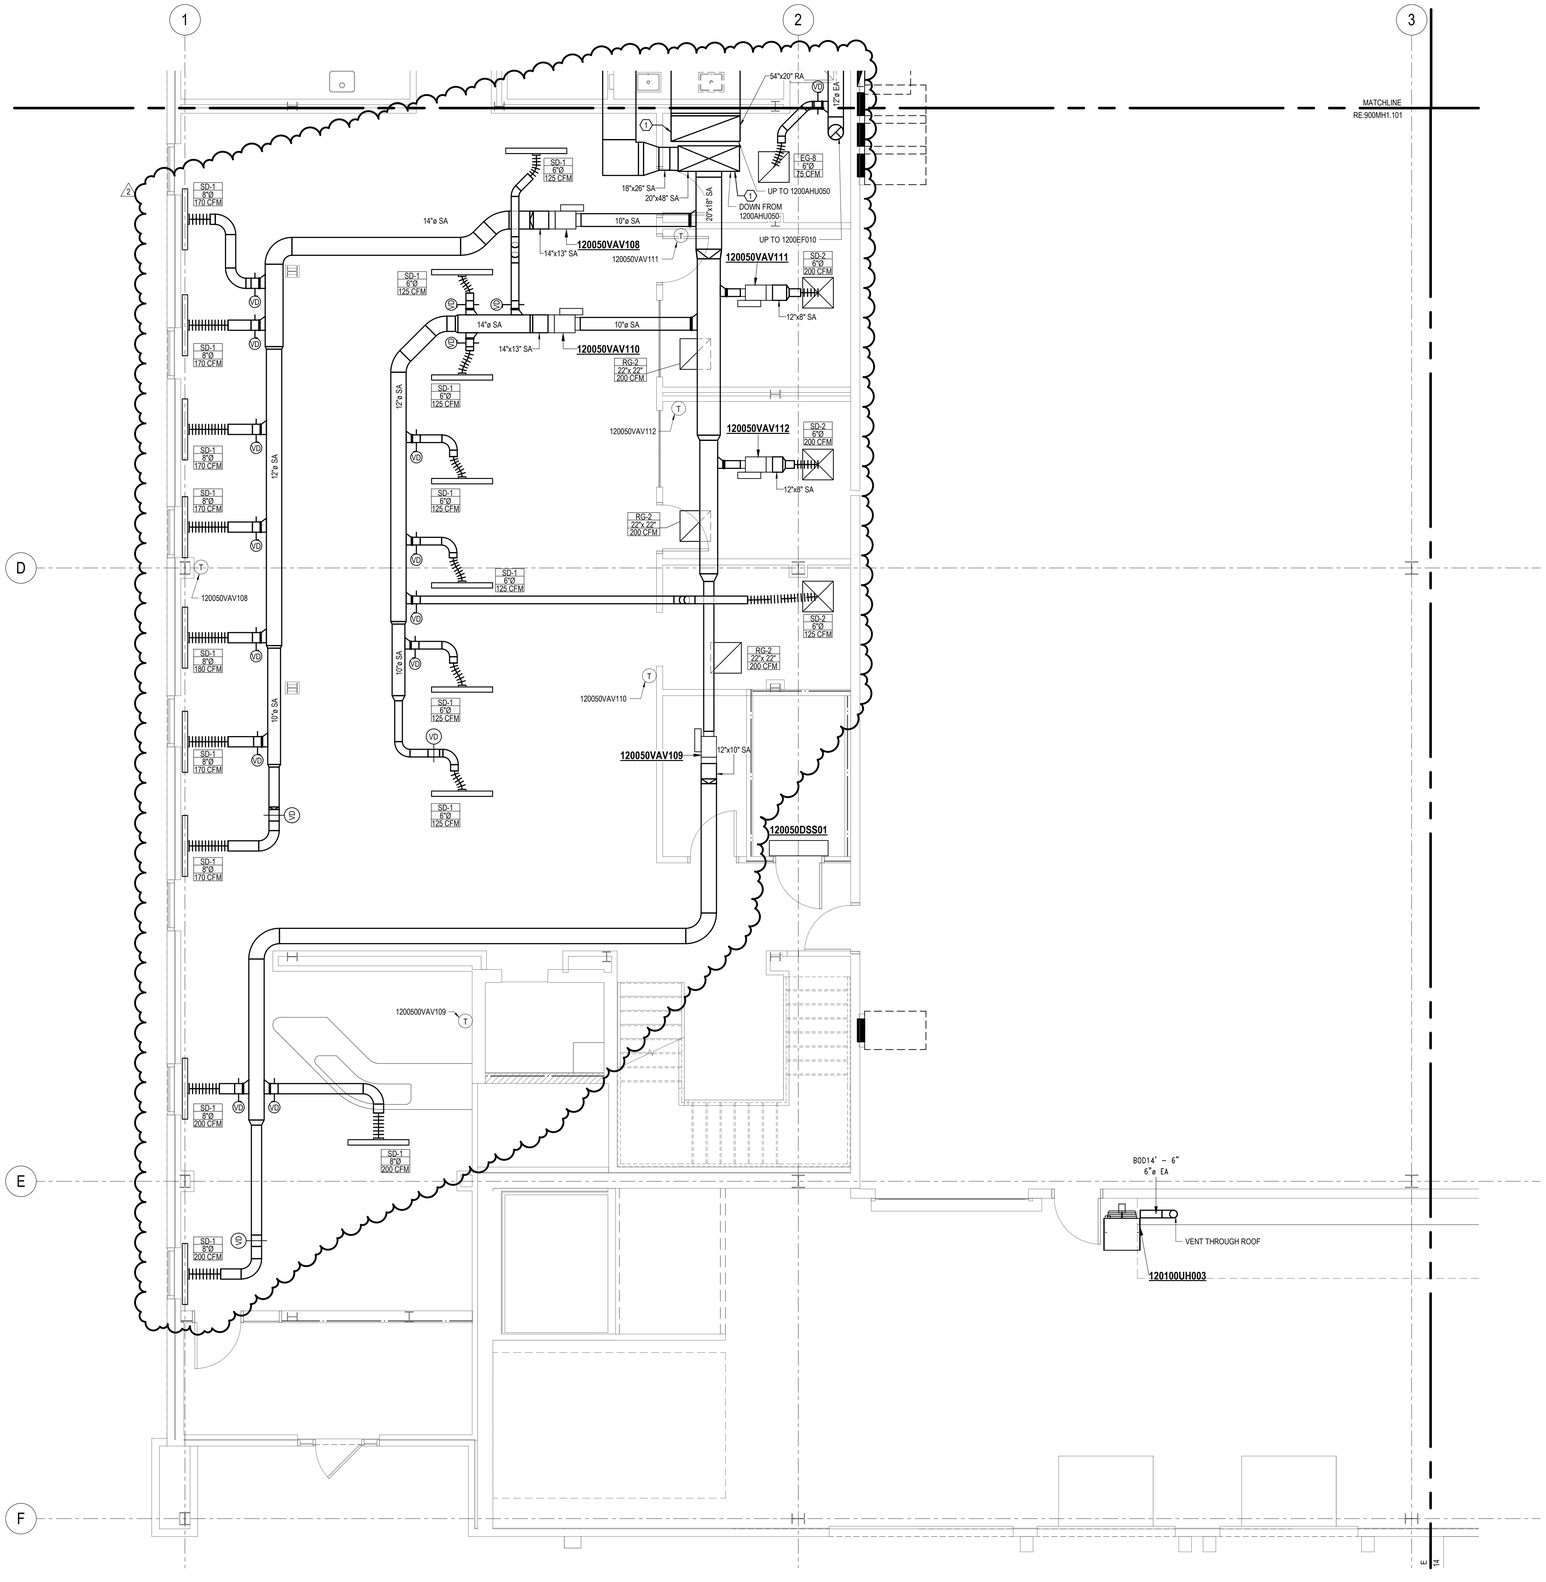

1
2
3
D
E
F
MATCHLINE
RE:900MH1.101
54"x20" RA
17"ø EA
EG-8
6"Ø
75 CFM
18"x26" SA
20"x48" SA
UP TO 1200AHU050
DOWN FROM
1200AHU050
20"x16" SA
UP TO 1200EF010
14"ø SA
10"ø SA
120050VAV108
14"x13" SA
120050VAV111
120050VAV111
SD-2
6"Ø
200 CFM
12"x8" SA
SD-1
6"Ø
125 CFM
SD-1
8"Ø
170 CFM
120050VAV110
RG-2
22"x 22"
200 CFM
12"ø SA
120050VAV112
120050VAV112
12"x8" SA
120050VAV108
SD-1
8"Ø
180 CFM
10"ø SA
120050VAV110
120050VAV109
12"x10" SA
120050DSS01
1200500VAV109
SD-1
8"Ø
200 CFM
BOD14' - 6"
6"ø EA
VENT THROUGH ROOF
120100UH003