K. ALL DUCT SEAMS SHALL BE SEALED.

L. ALL CEILING DIFFUSERS SHALL HAVE A MINIMUM 2'-0" LENGTH OF FLEXIBLE DUCT FOR SOUND DAMPENING. DO NOT USE FLEX DUCT TO CHANGE DIRECTION.

M. KEEP ALL DUCT OPENINGS AND AIR DEVICES COVERED AIR-TIGHT UNTIL ALL DUST CREATING ACTIVITY HAS BEEN FINISHED AND EQUIPMENT IS READY FOR START-UP.

N. DUCTWORK TO DIFFUSER SHALL MATCH DIFFUSER NECK SIZE UNLESS NOTED OTHERWISE.

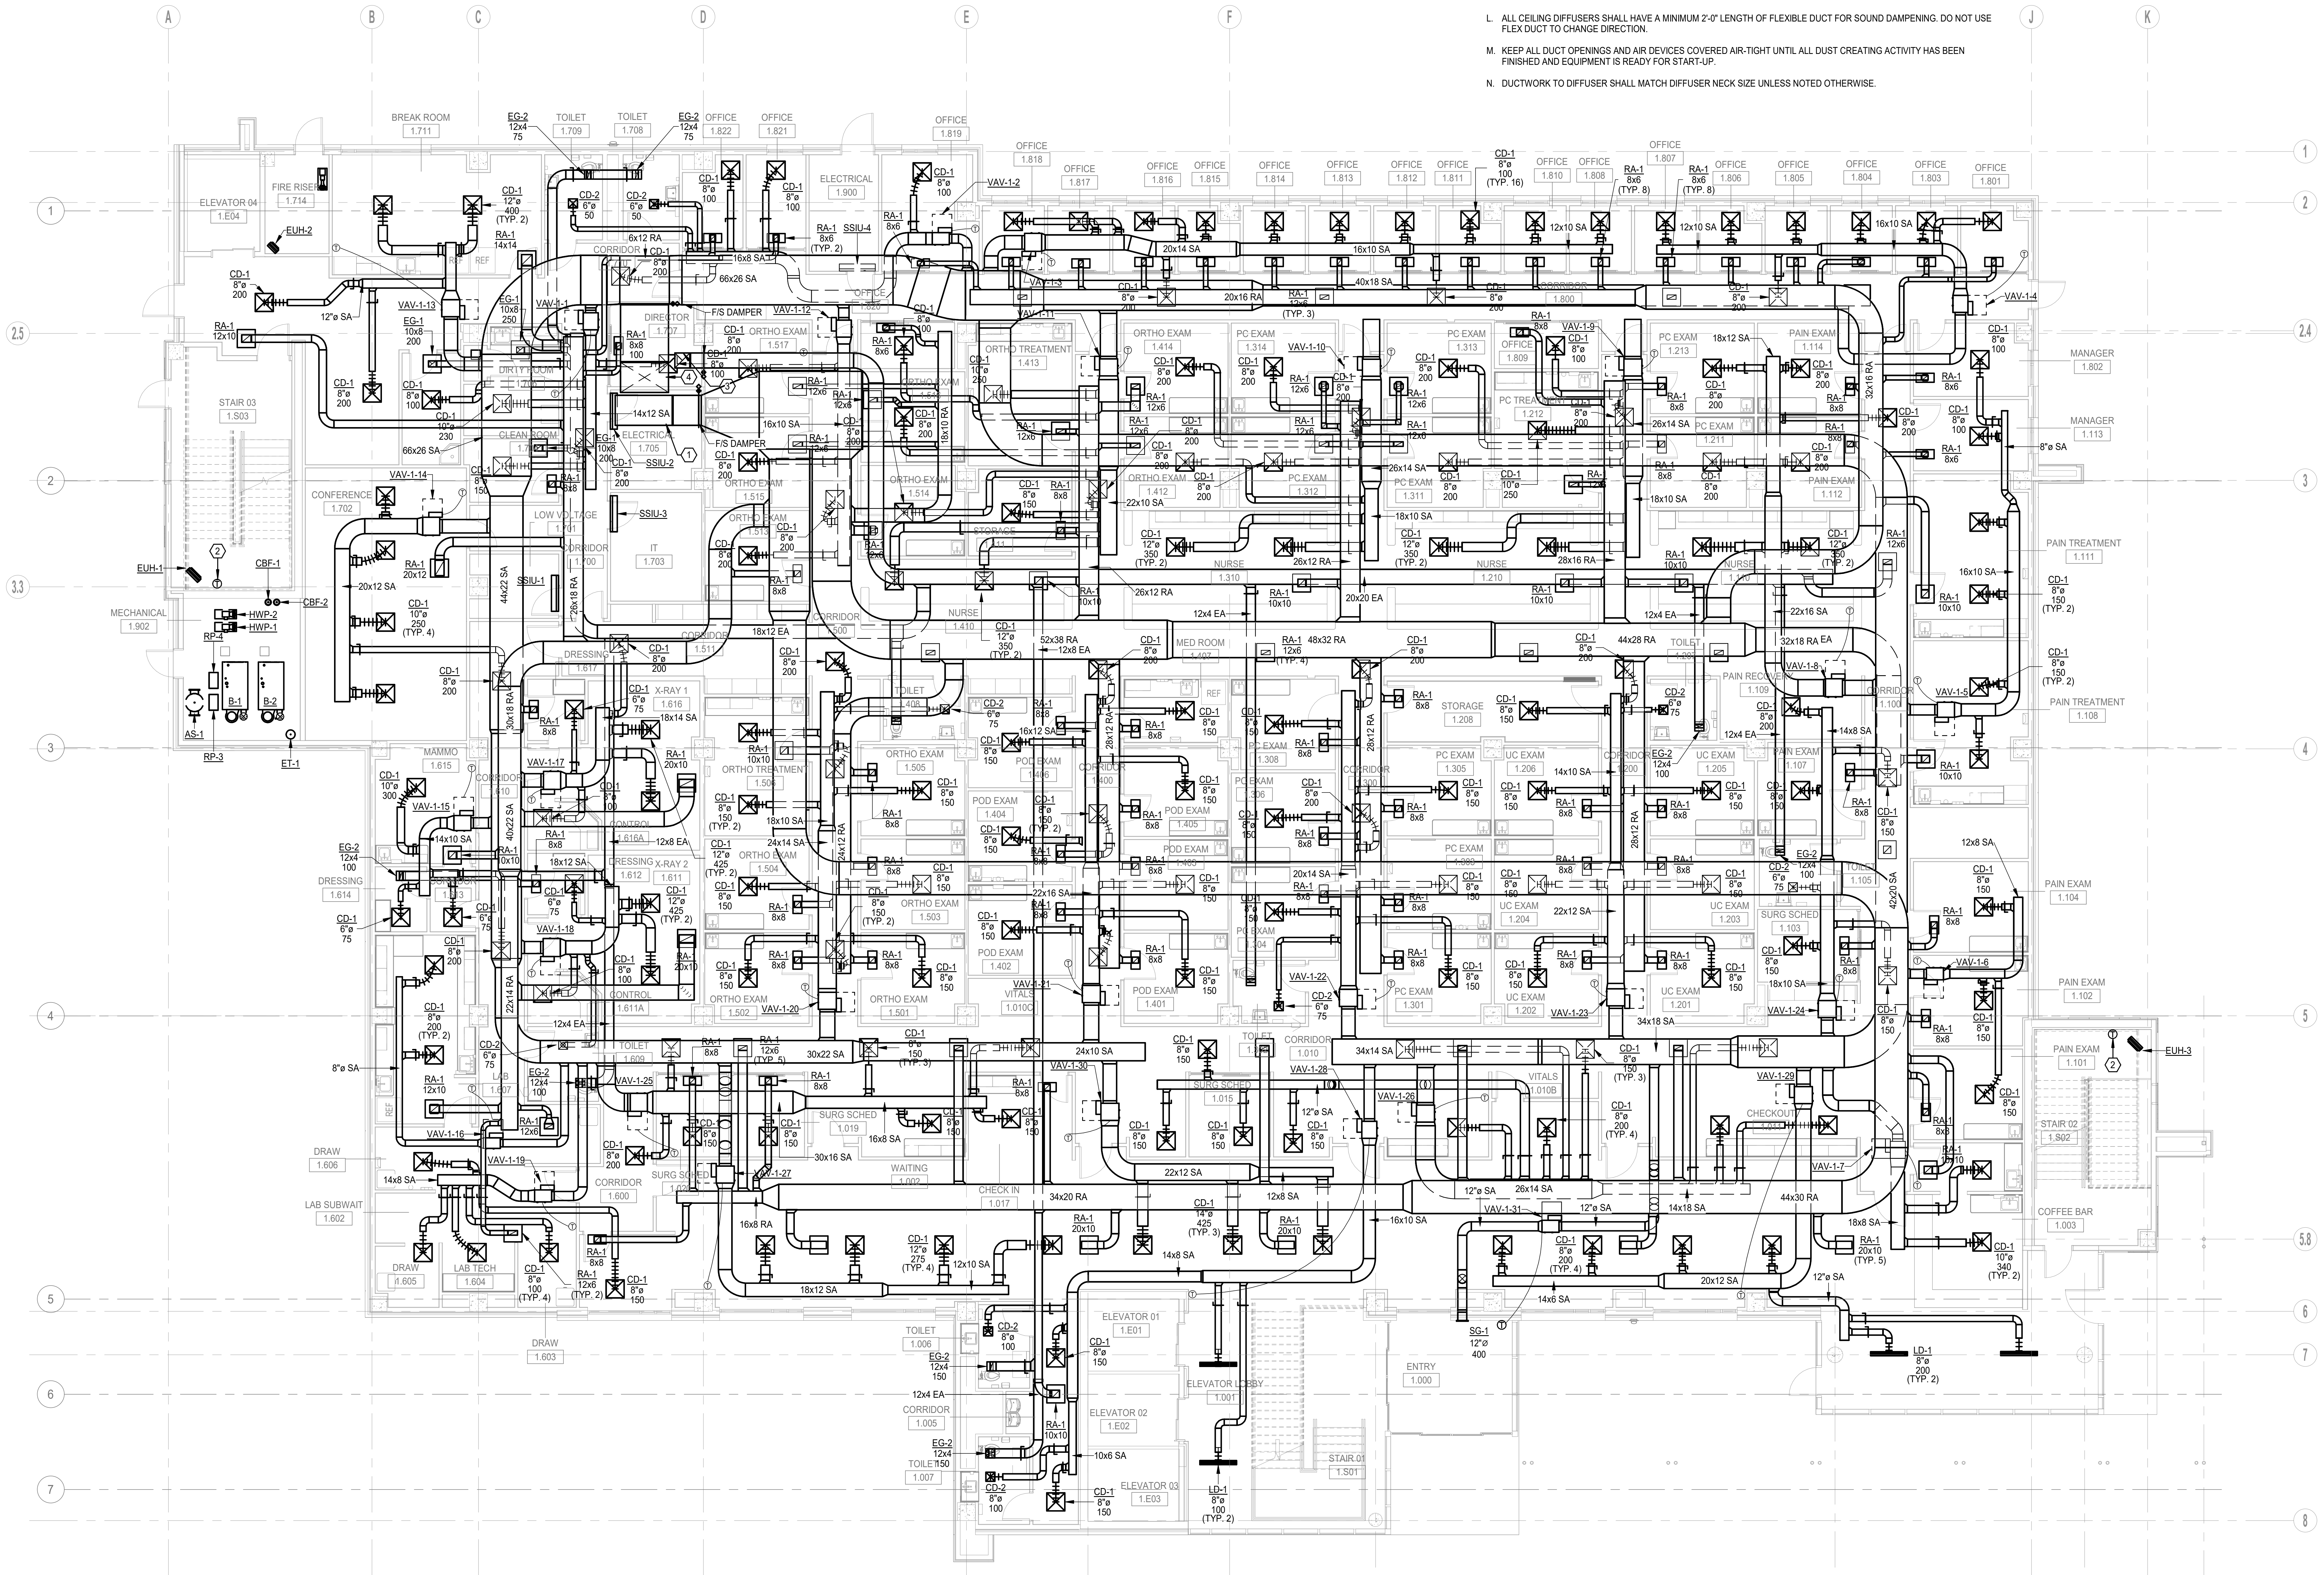
A
B
C
D
E
F
J
K
1
2
2.5
2.4
3
3.3
4
5
5.8
6
7
8
BREAK ROOM 1.711
TOILET 1.709
TOILET 1.708
OFFICE 1.822
OFFICE 1.821
OFFICE 1.819
ELECTRICAL 1.900
ELEVATOR 04 1.E04
FIRE RISER 1.714
STAIR 03 1.S03
CONFERENCE 1.702
MECHANICAL 1.902
MAMMO 1.615
DRESSING 1.614
DRAW 1.606
LAB SUBWAIT 1.602
DRAW 1.605
LAB TECH 1.604
DRAW 1.603
ELEVATOR 01 1.E01
ELEVATOR 02 1.E02
ELEVATOR 03 1.E03
ELEVATOR LOBBY 1.001
ENTRY 1.000
STAIR 01 1.S01
STAIR 02 1.S02
COFFEE BAR 1.003
MANAGER 1.802
MANAGER 1.113
PAIN TREATMENT 1.111
PAIN TREATMENT 1.108
PAIN EXAM 1.104
PAIN EXAM 1.102
PAIN EXAM 1.101
EUH-1
EUH-2
EUH-3
CBF-1
CBF-2
HWP-1
HWP-2
B-1
B-2
AS-1
RP-3
ET-1